REVISÃO DA PRANCHA	DATA	EMITIDO POR	DESCRIÇÃO
	01.02.16	JÚLIO	PROJETO LEGAL
	15.02.16	BIANCA	CORREÇÕES COM BASE NA NOTIFICAÇÃO DE 08.03.16
0	03.03.17	MARIACHRISTINA	EMISSÃO DE PROJETO LEGAL
1	06.11.17	SHAIANE	COMPATIBILIZAÇÃO INSTALAÇÕES E PRESSURIZAÇÃO

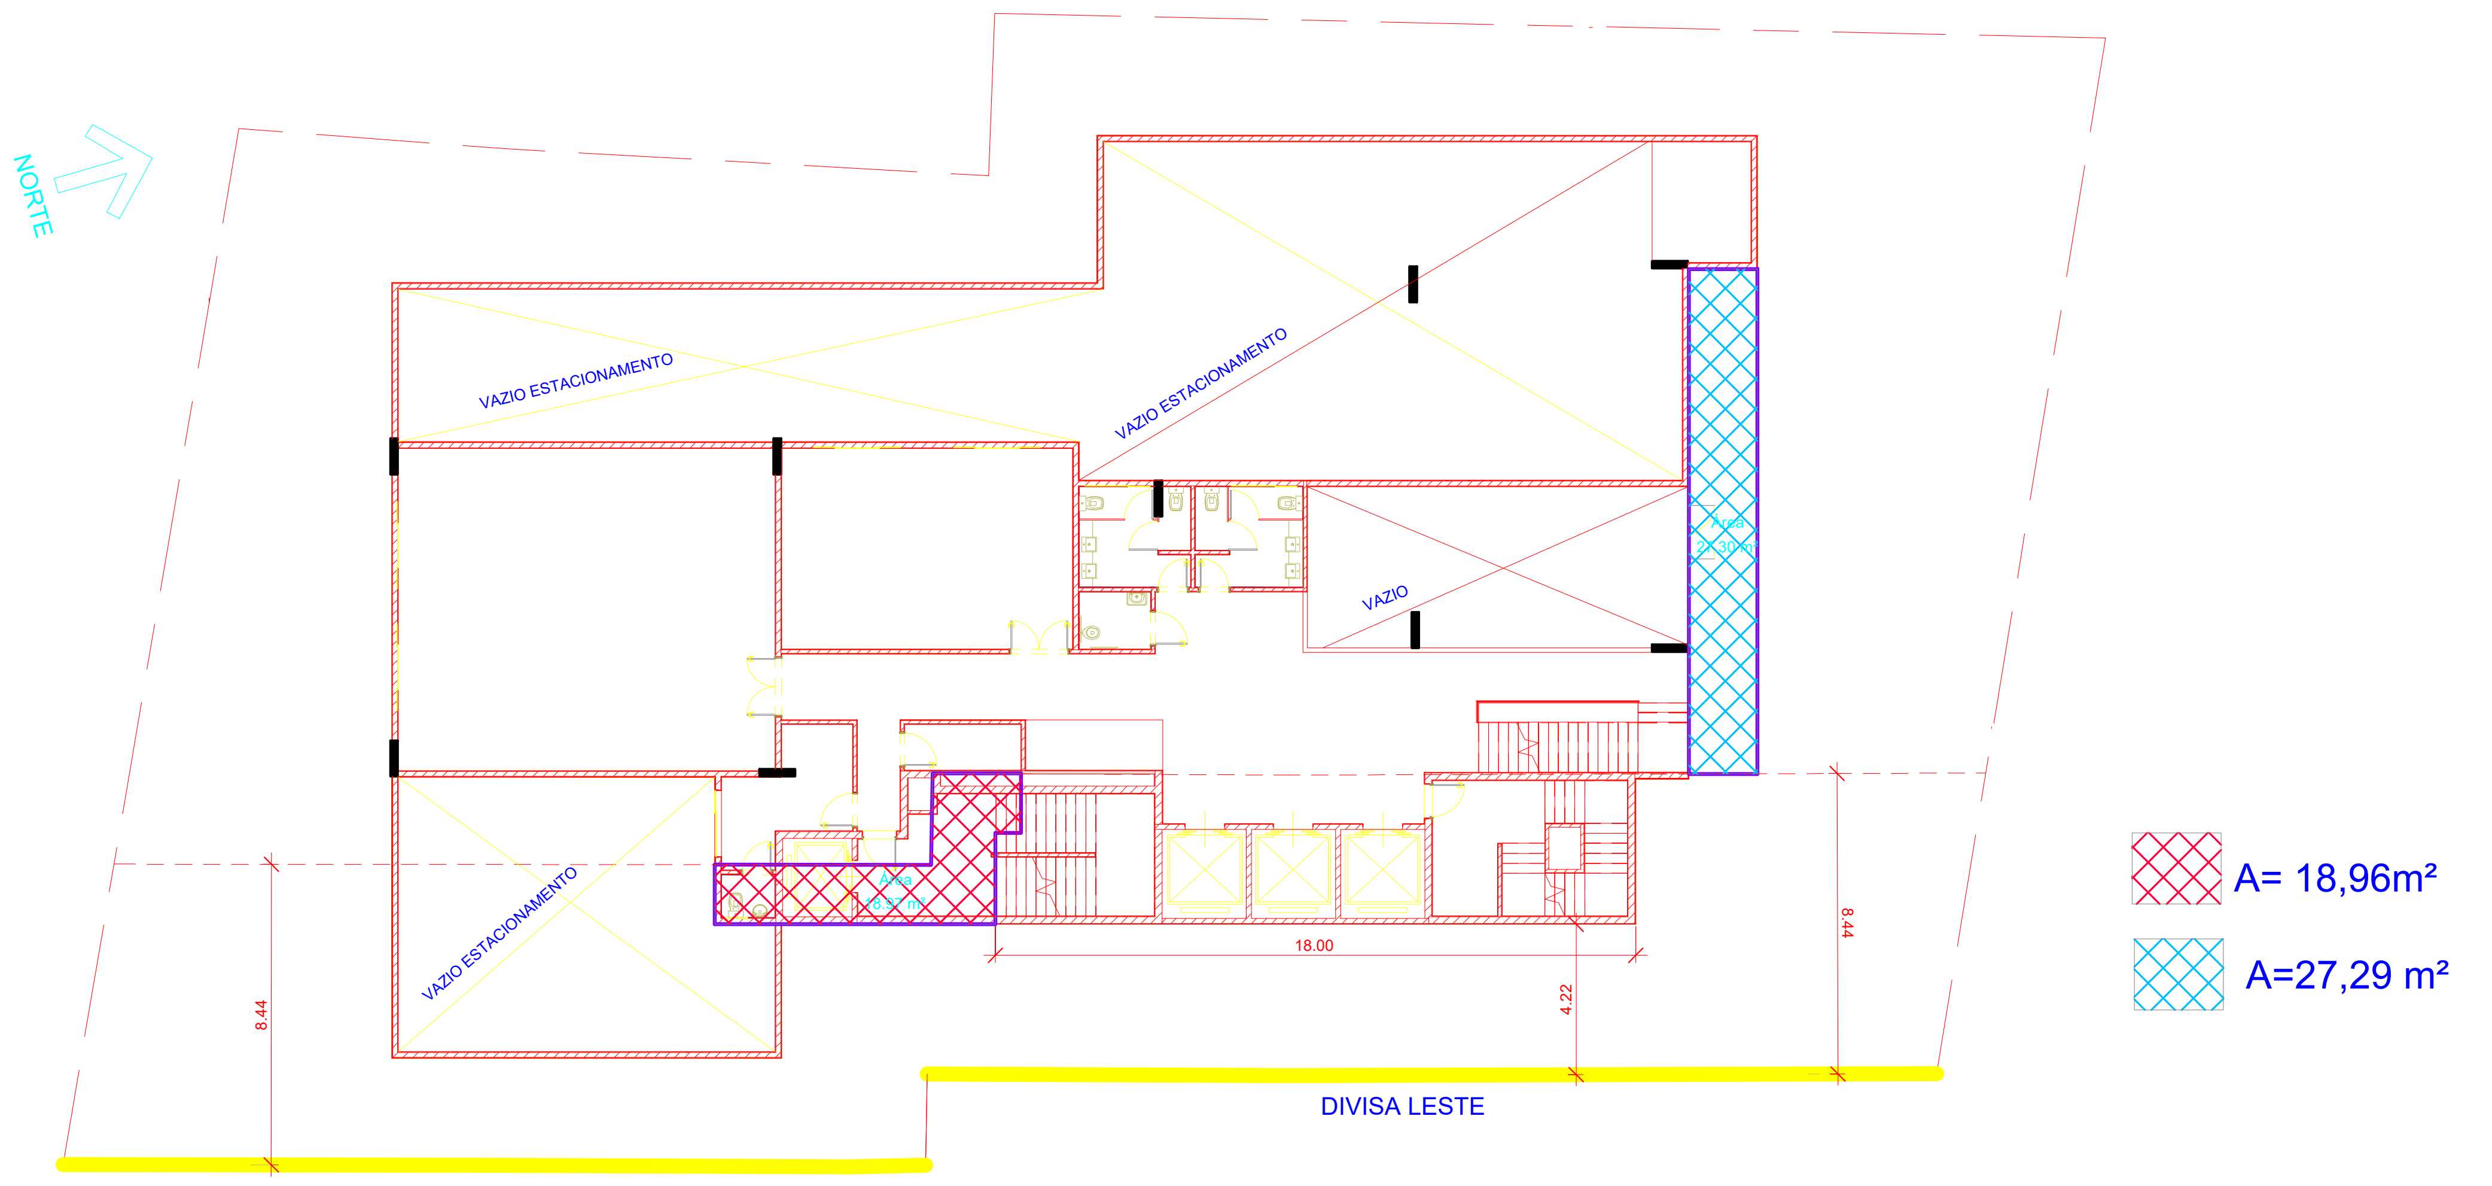

2 AFASTAMENTO MÉDIO LESTE - MEZANINO - CONVENÇÕES
ESC.: 1 : 200

QUADRO PELES DE VIDRO - MEZANINO

Nº ESQ.	LARGURA	ALTURA
PV7	7.975	7.740

QUADRO DE PORTAS - MEZANINO

ESQUADRIA	LARGURA	ALTURA
PCF	0.900	2.100
PM2	0.800	2.100
PM3	0.900	2.100
PM5	1.600	2.100

QUADRO DE JANELAS - MEZANINO

ESQUADRIA	LARGURA	ALTURA	PEITORIL
JA1	0.600	0.600	1.600
JA3	1.800	0.400	1.100
JA4	2.400	0.600	1.600
JA5	1.800	0.600	1.600

ISS - CÁLCULO

ISS - CONSTRUÇÃO

ISS - PROJETO

ISS - PROJETO

SUP	COD. ATIVIDADE	INSCRIÇÃO	F/J
01	0625.8	56.125-8	J

Firma: NASSER HISSA ARQ. ASSOCIADOS S/S LTDA
Local: Av. Barão de Studart, 215 - Meireles

ISS - PROJETO

CREA

APROVO

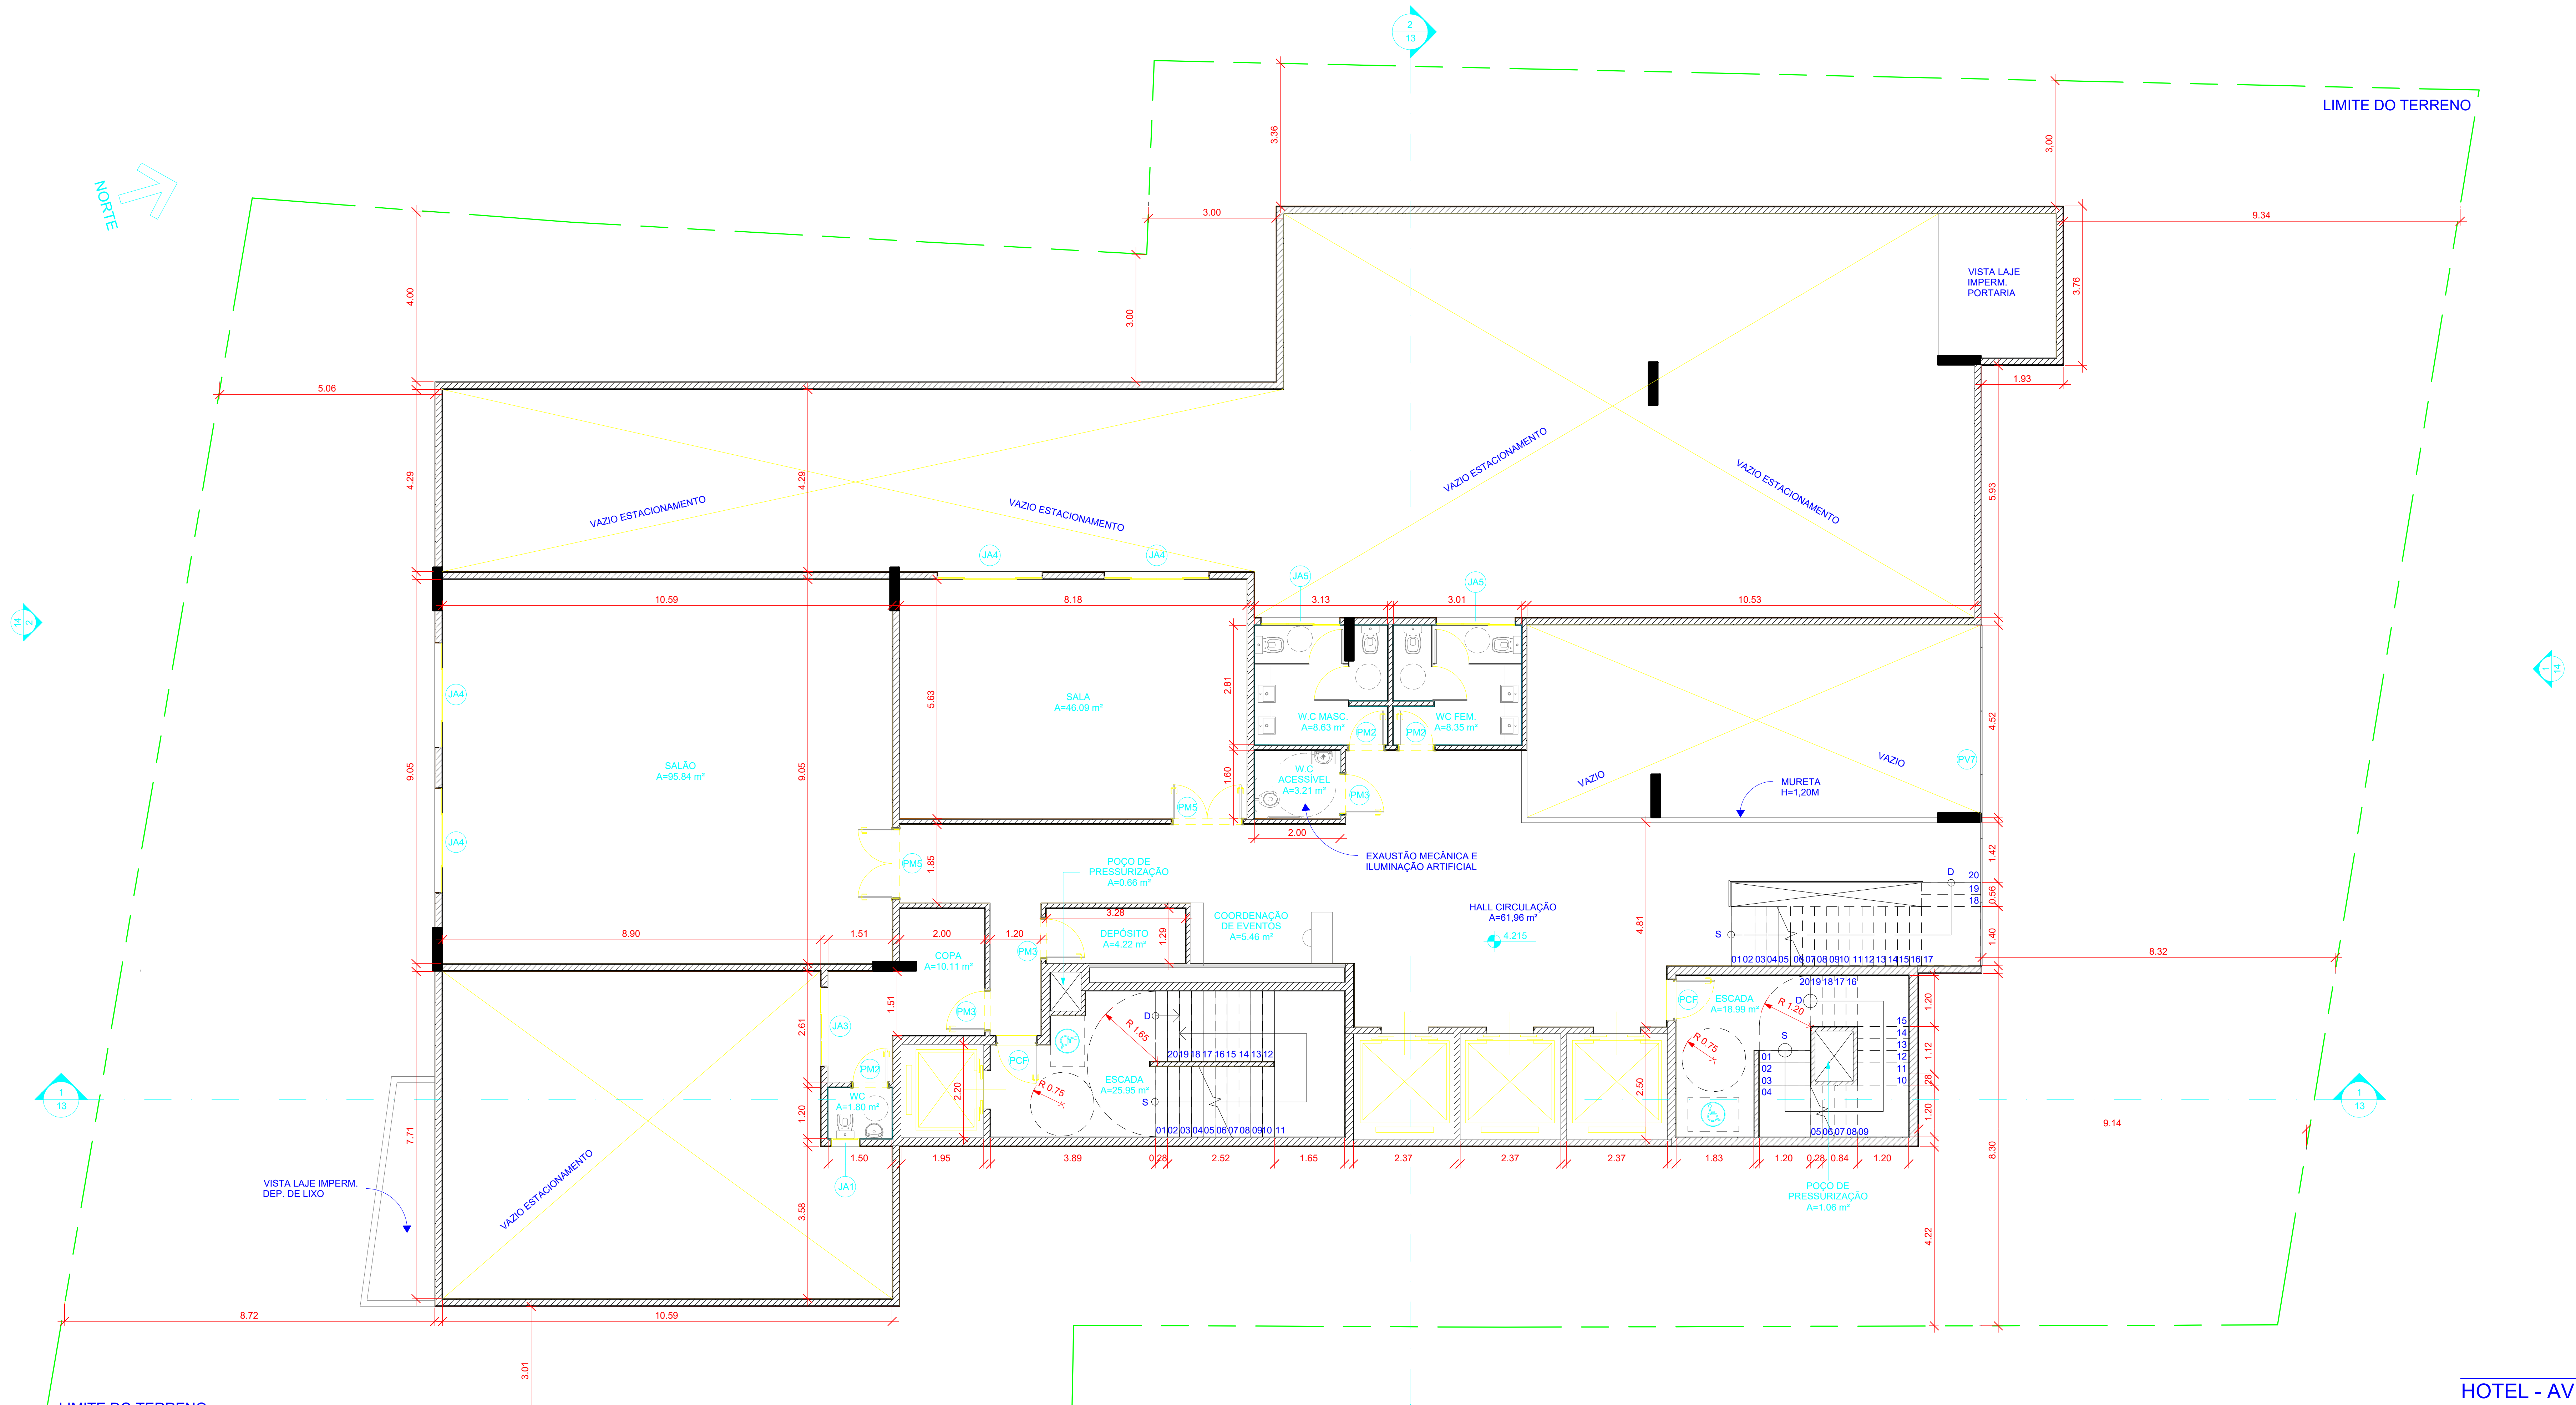

1 MEZANINO - CONVENÇÕES
ESC.: 1 : 100

PROPRIETÁRIO

PROJETO NASSER HISSA ARQUITETOS ASSOCIADOS S/S LTDA
CNPJ: 05.612.106/0001-60

CÁLCULO

CONSTRUÇÃO

HOTEL - AVENIDA BEIRA MAR
HOTEL - COD.: 55.11.51 - PGT1

08
MEZANINO - CONVENÇÕES
DATA: 06/11/2017 17:09:46
PROJ.: 14-009

NASSER HISSA
ARQUITETOS ASSOCIADOS
www.nasserhissa.com.br
Av. Barão de Studart, 215
e-mail: tecnica@nasserhissa.com.br
Fortaleza Ce. BRASIL 60120-000

T:\PRO\2014\14-009 - HOTEL-SILVIO FROTA - SIMPEX - AV. BEIRA MAR\PROJETO LEGAL\OPÇÃO 09\14_009-HSF-PL-30.10.17.rvt

Informações.:Biblioteca 02