REVISÃO DA PRANCHA	DATA	EMITIDO POR	DESCRIÇÃO
	01.02.16	JULIO	PROJETO LEGAL
	15.02.16	BIANCA	CORREÇÕES COM BASE NA NOTIFICAÇÃO DE 08.03.16
0	03.03.17	MARIACHRISTINA	EMISSÃO DE PROJETO LEGAL
1	06.11.17	SHAIANE	COMPATIBILIZAÇÃO INSTALAÇÕES E PRESSURIZAÇÃO

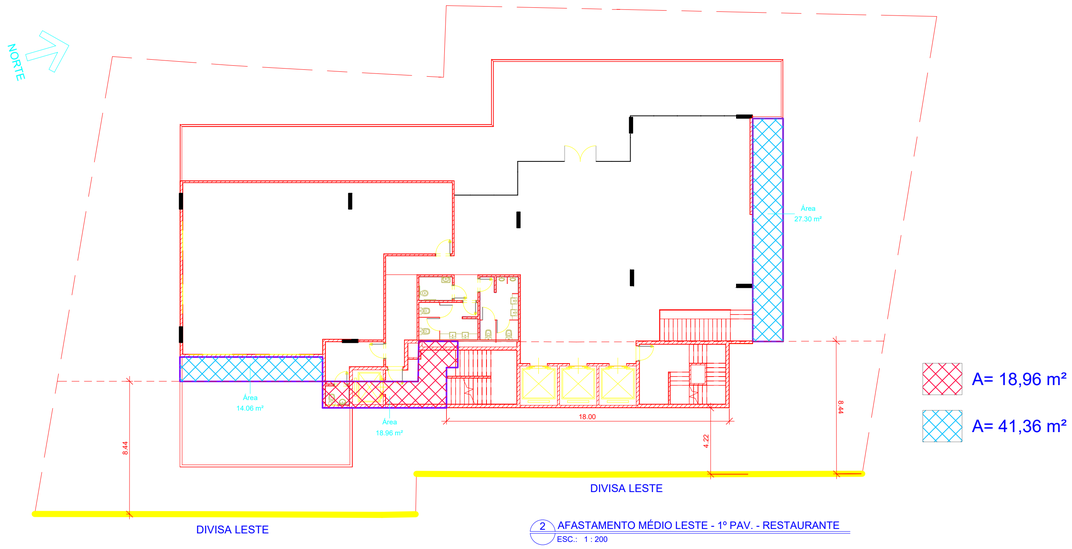

A= 18,96 m²

A= 41,36 m²

2 AFASTAMENTO MÉDIO LESTE - 1º PAV. - RESTAURANTE
ESC.: 1 : 200

QUADRO PELES DE VIDRO - 1º PAVIMENTO

Nº ESQ.	LARGURA	ALTURA
PV1	7.975	3.500
PV2	6.727	3.000
PV3	1.679	3.000
PV4	7.145	3.000
PV5	2.097	3.000
PV6	3.970	3.600

QUADRO DE PORTAS - 1º PAVIMENTO

ESQUADRIA	LARGURA	ALTURA
PCF	0.900	2.100
PM2	0.800	2.100
PM3	0.900	2.100

QUADRO DE JANELAS - 1º PAVIMENTO

ESQUADRIA	LARGURA	ALTURA	PEITORIL
JA1	0.600	0.600	1.600
JA4	2.400	0.600	1.600
JA7	3.600	0.600	1.600

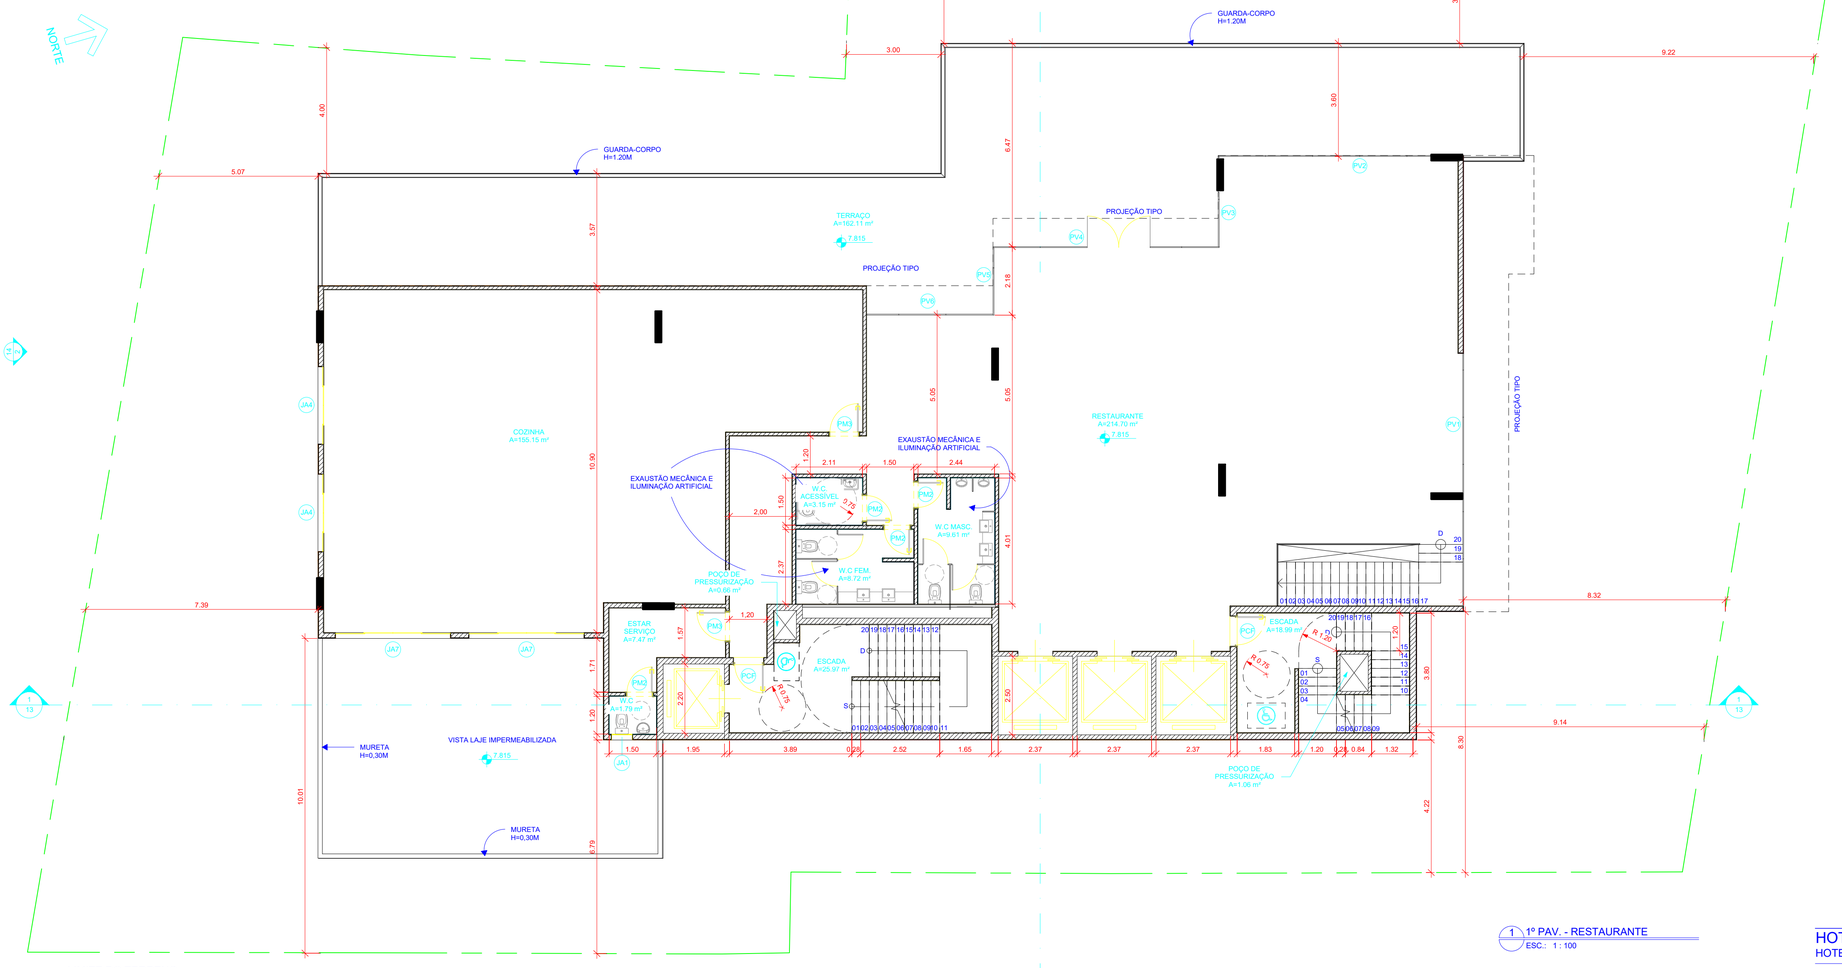

1 1º PAV. - RESTAURANTE
ESC.: 1 : 100

ISS - CÁLCULO

ISS - CONSTRUÇÃO

ISS - PROJETO

ISS - PROJETO

SUP	COD. ATIVIDADE	INSCRIÇÃO	F/J
01	0625.8	56.125-8	J

Firma: NASSER HISSA ARQ. ASSOCIADOS S/S LTDA
Local: Av. Barão de Studart, 215 - Meireles

ISS - PROJETO

CREA

APROVO

PROPRIETÁRIO

PROJETO NASSER HISSA ARQUITETOS ASSOCIADOS S/S LTDA
CNPJ: 05.612.106/0001-60

CÁLCULO

CONSTRUÇÃO

HOTEL - AVENIDA BEIRA MAR

HOTEL - COD.: 55.11.51 - PGT1

09 1º PAV. - RESTAURANTE

DATA: 06/11/2017 17:09:51

PROJ.: 14-009

NASSER HISSA ARQUITETOS ASSOCIADOS
www.nasserhissa.com.br
Av. Barão de Studart, 215
e-mail: tecnica@nasserhissa.com.br
Fortaleza Ce. BRASIL 60120-000