


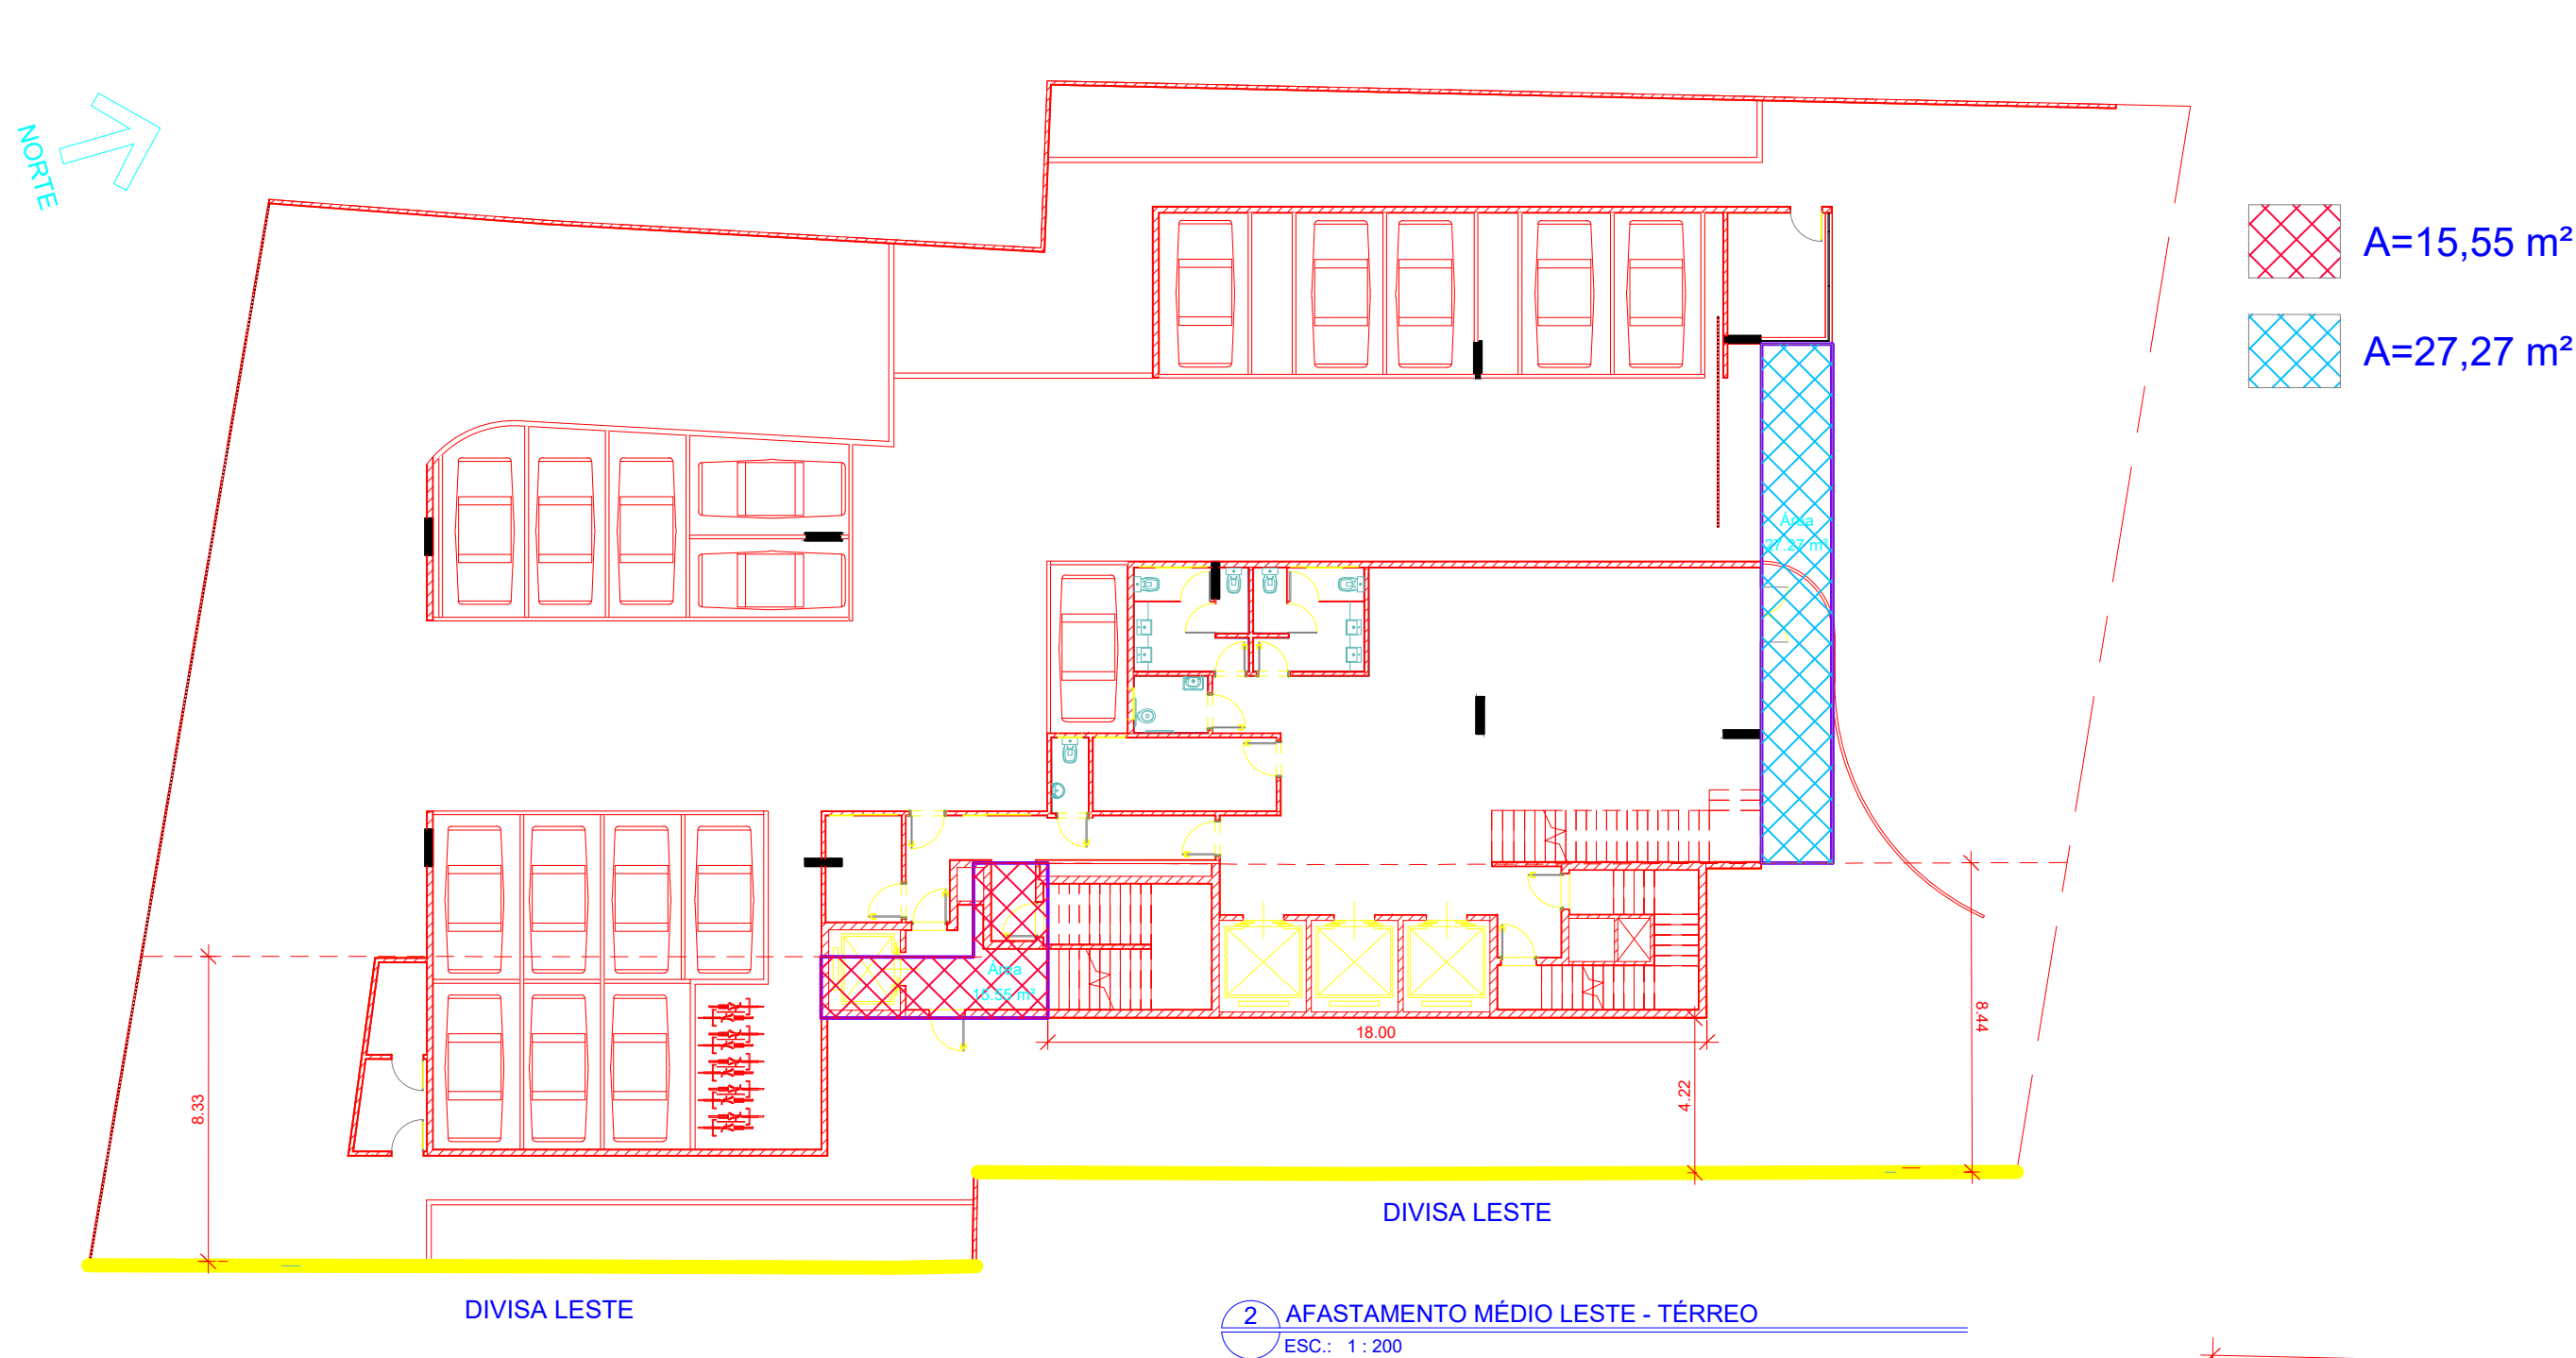

REVISÃO DA PRANCHA	DATA	EMITIDO POR	DESCRIÇÃO
01	03.02.16	JALCO	PROJETO LEGAL
02	15.02.16	BIANCA	CORREÇÕES COM BASE NA NOTIFICAÇÃO DE 08.03.16
03	15.02.16	BARBARA M.	CORREÇÃO TAMANHO CARGA E DESCARGA
04	28.03.16	BARBARA M.	ACRESCENDO BLOCOS E TAPETE
05	03.03.17	MARIACHRISTINA	EMISSÃO DE PROJETO LEGAL
06	08.11.17	SHIANE	COMPATIBILIZAÇÃO INSTALAÇÕES E PRESSURIZAÇÃO

QUADRO DE PORTAS - TÉRREO		
ESQUADRIA	LARGURA	ALTURA
PA3	0.800	2.200
PCF	0.900	2.100
PM2	0.800	2.100
PM3	0.900	2.100

QUADRO DE JANELAS - TÉRREO			
ESQUADRIA	LARGURA	ALTURA	PEITORIL
JAT	0.600	0.600	1.600
JAS	1.800	0.600	1.600
JAB	0.800	0.600	1.600
JAT0	1.800	0.600	1.600

QUADRO PELES DE VIDRO - TÉRREO		
Nº ESQ.	LARGURA	ALTURA
PV7	7.975	7.740
PV8	1.779	2.640
PV9	3.452	2.640

ISS - CÁLCULO

ISS - CONSTRUÇÃO

ISS - PROJETO

ISS - PROJETO

SUP	COD. ATIVIDADE	INSCRIÇÃO	FUJ
01	0625.8	56.125-8	J

Firma: NASSER HISSA ARQ. ASSOCIADOS S/S LTDA
Local: Av. Barão de Studart, 215 - Meireles

ISS - PROJETO

CREA


APROVO

PROPRIETÁRIO

PROJETO NASSER HISSA ARQUITETOS ASSOCIADOS S/S LTDA
CNPJ: 05.612.106/0001-60

CÁLCULO

CONSTRUÇÃO

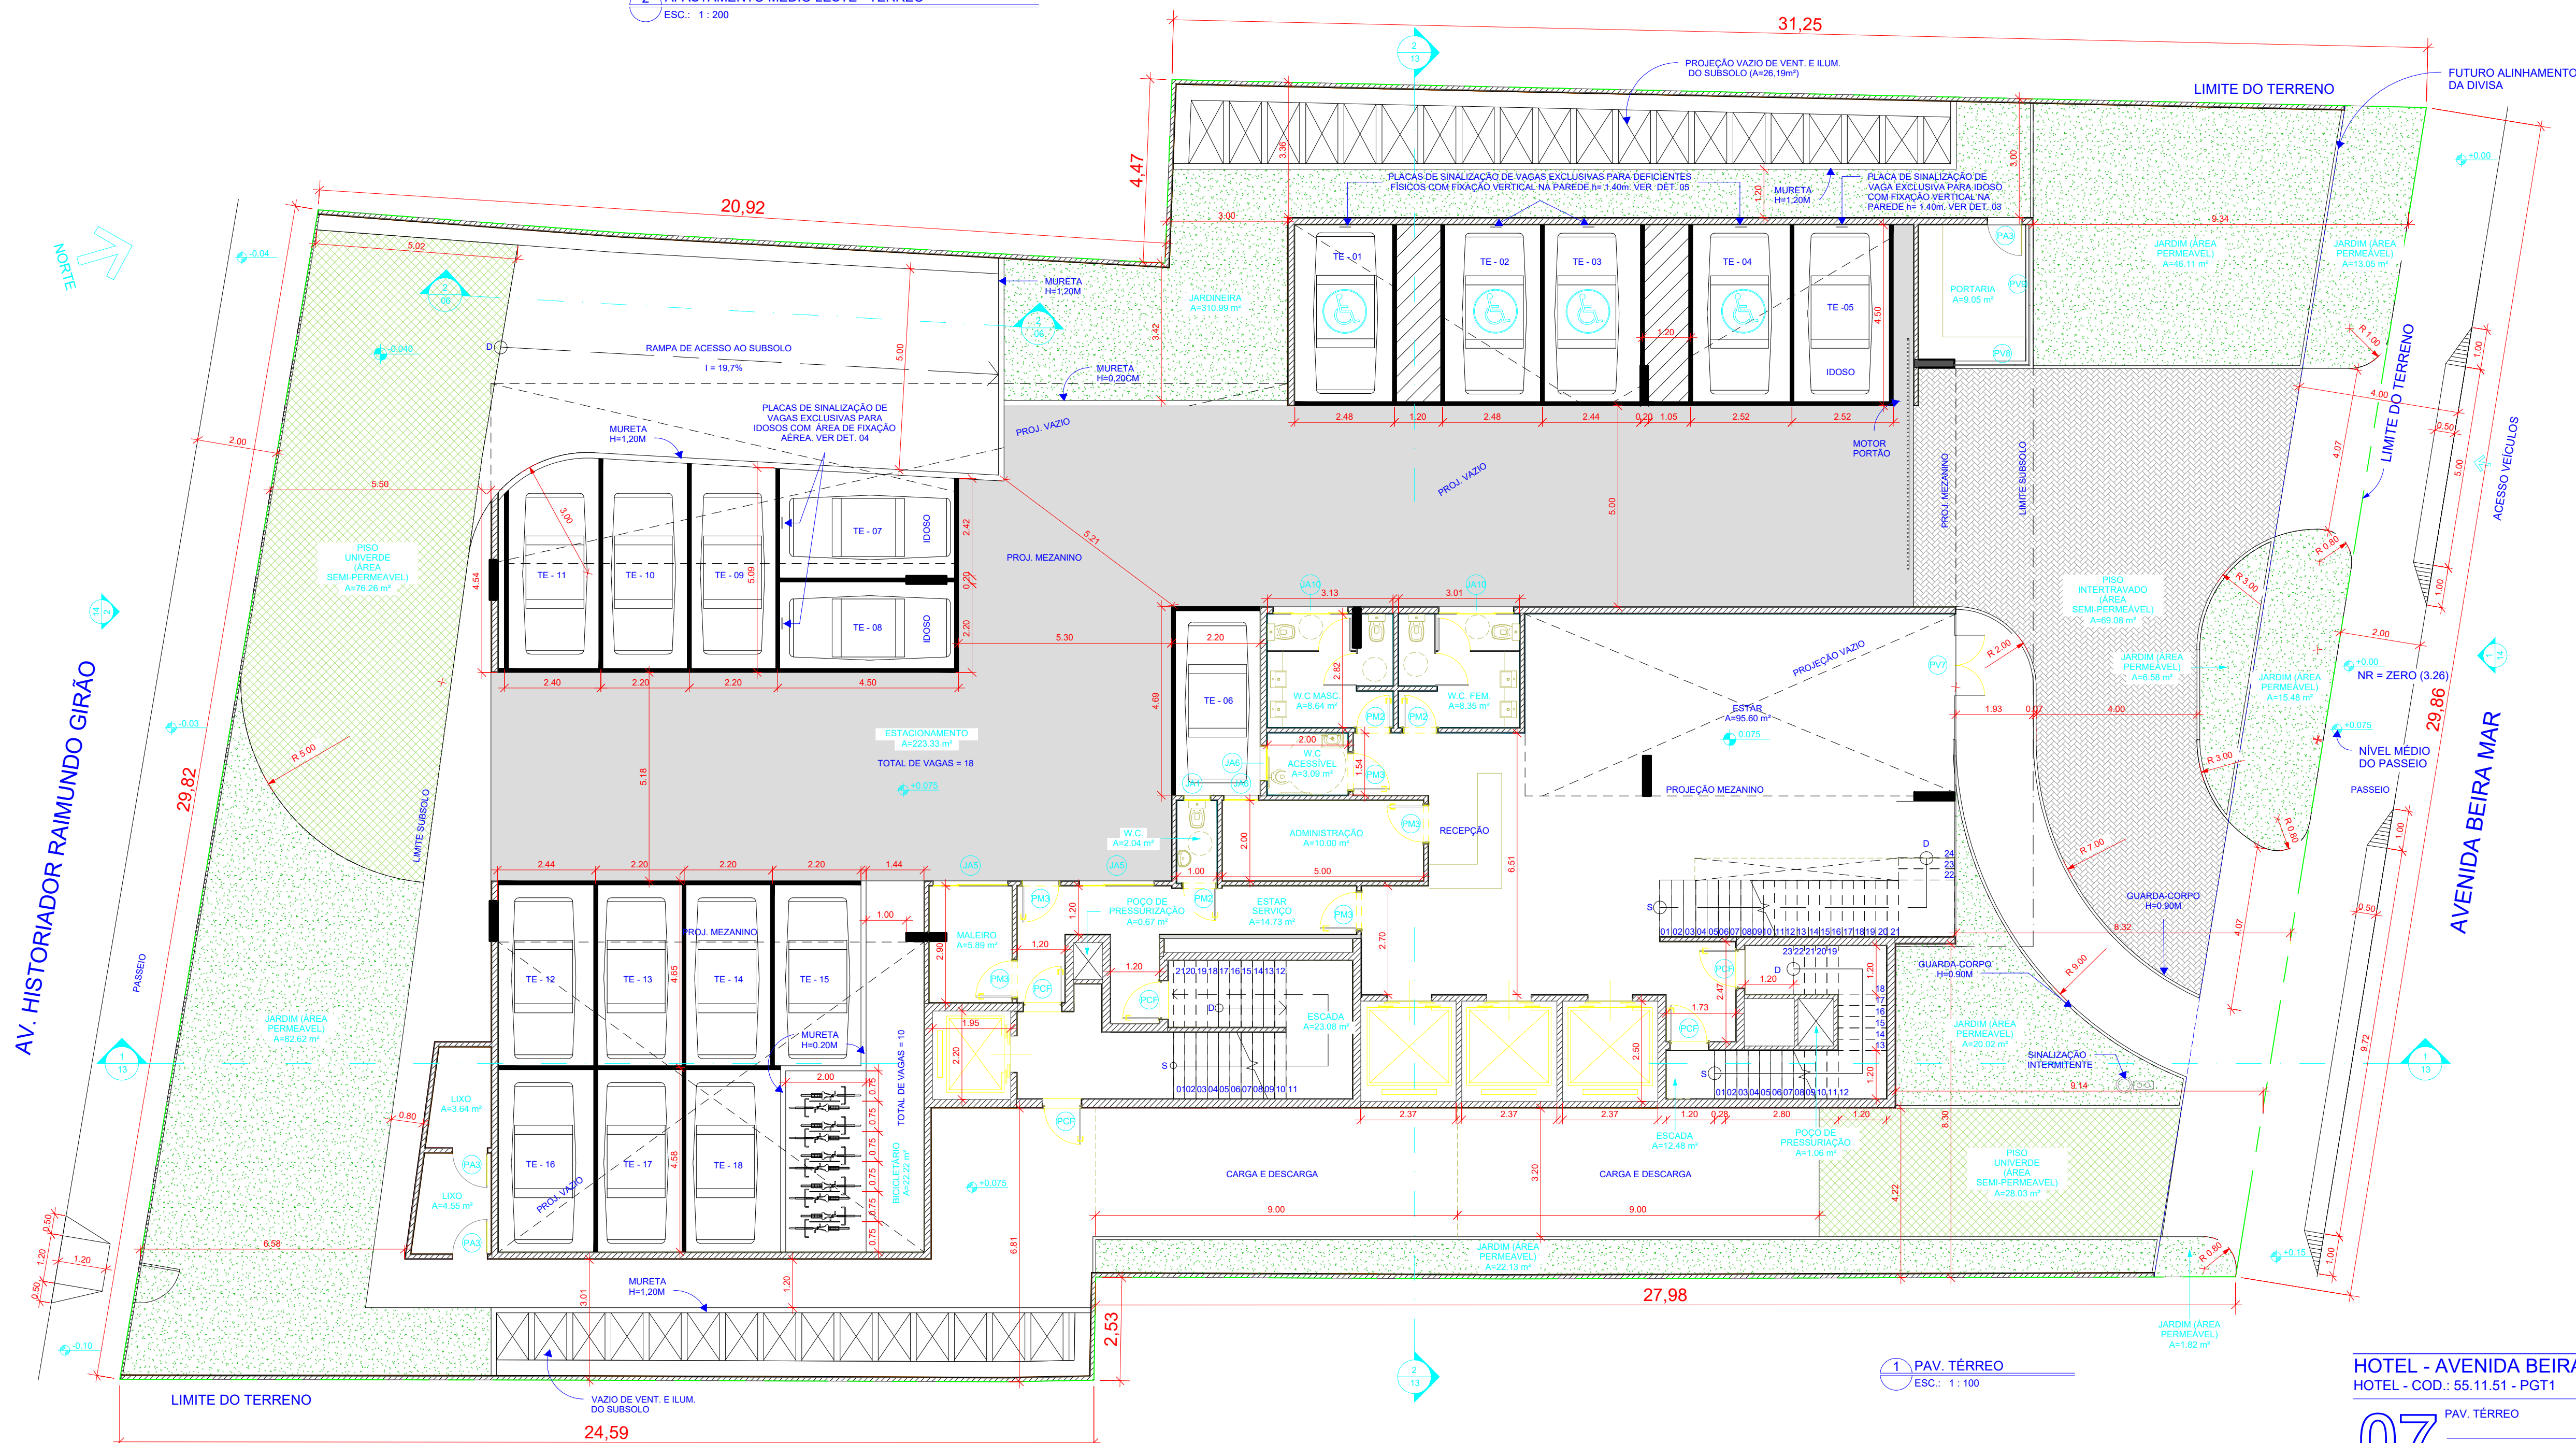

1 PAV. TÉRREO
ESC.: 1:100

HOTEL - AVENIDA BEIRA MAR
HOTEL - COD.: 55.11.51 - PGT1

07 PAV. TÉRREO
DATA: 06/11/2017 17:09:40
PROJ.: 14-009

NASSER HISSA
ARQUITETOS ASSOCIADOS

www.nasserhissa.com.br
e-mail: tecnico@nasserhissa.com.br
Fortaleza - CE, BRASIL 60120-000