

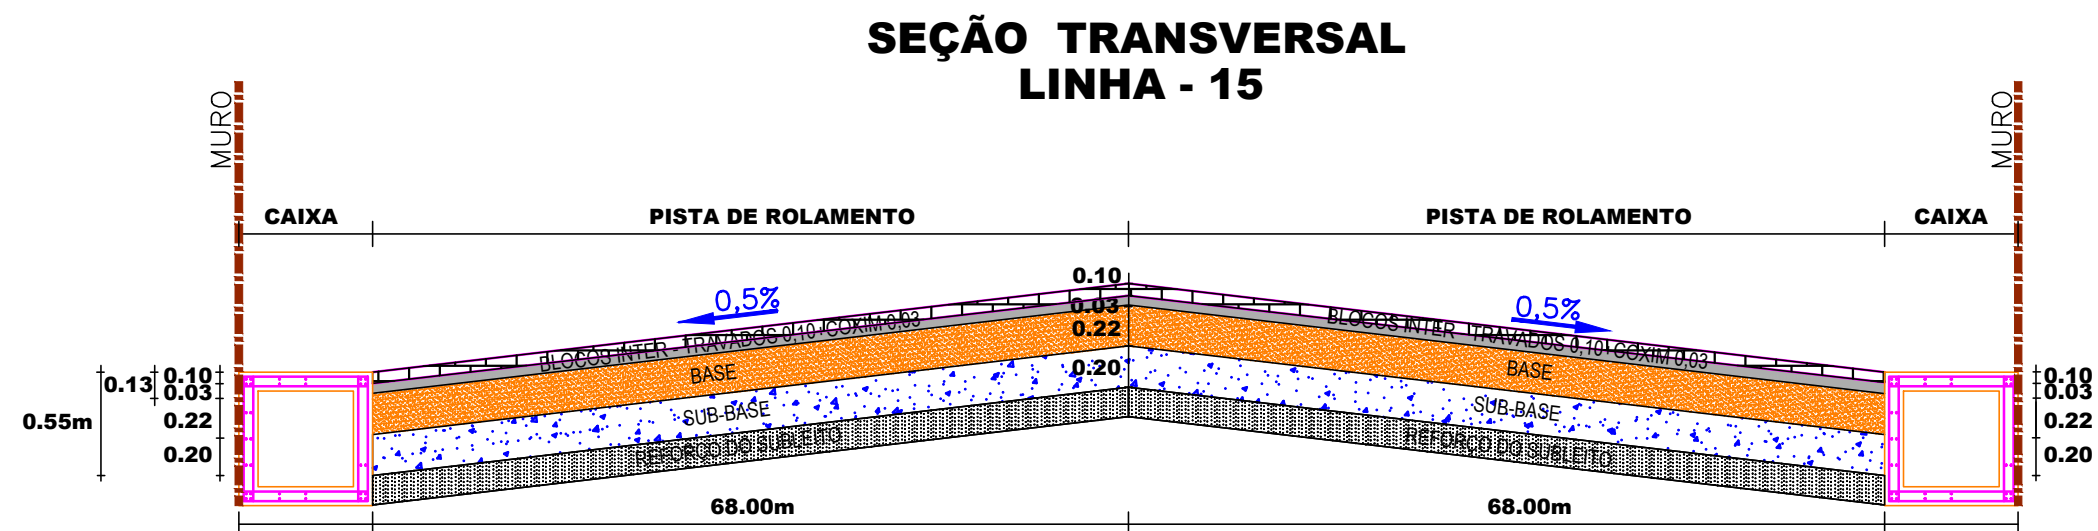


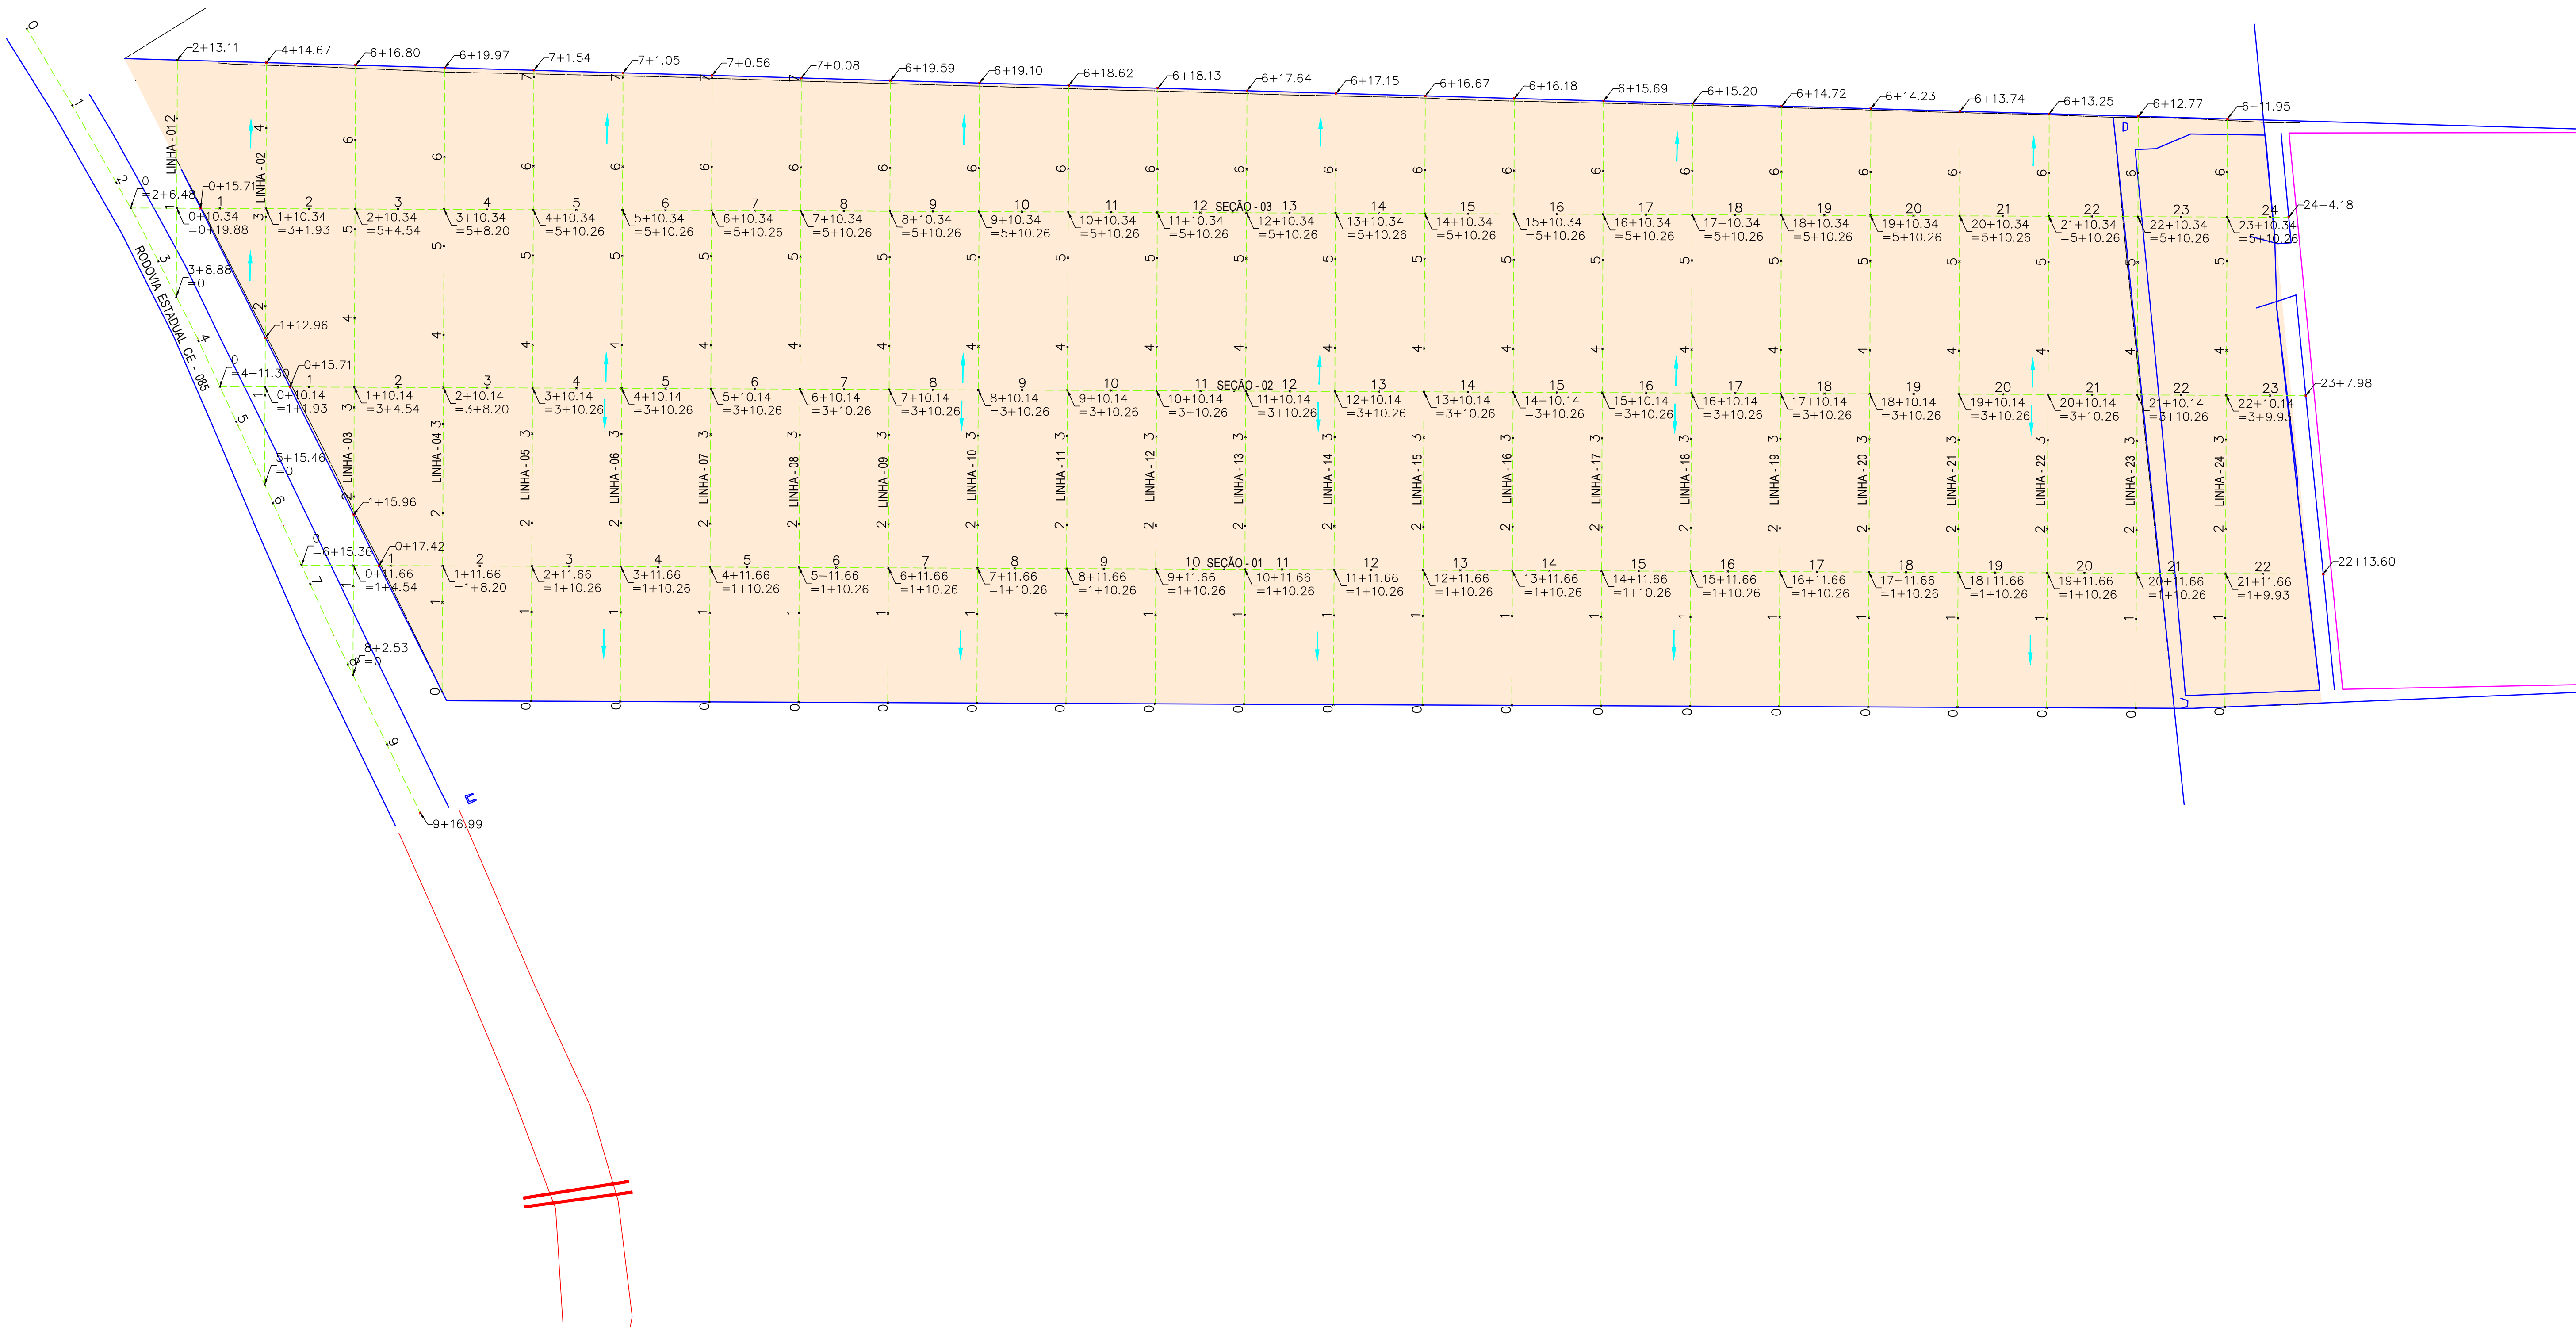

VIDE MEMORIAL DESCRITIVO PARA AS ESPECIFICAÇÕES
DA PAVIMENTAÇÃO

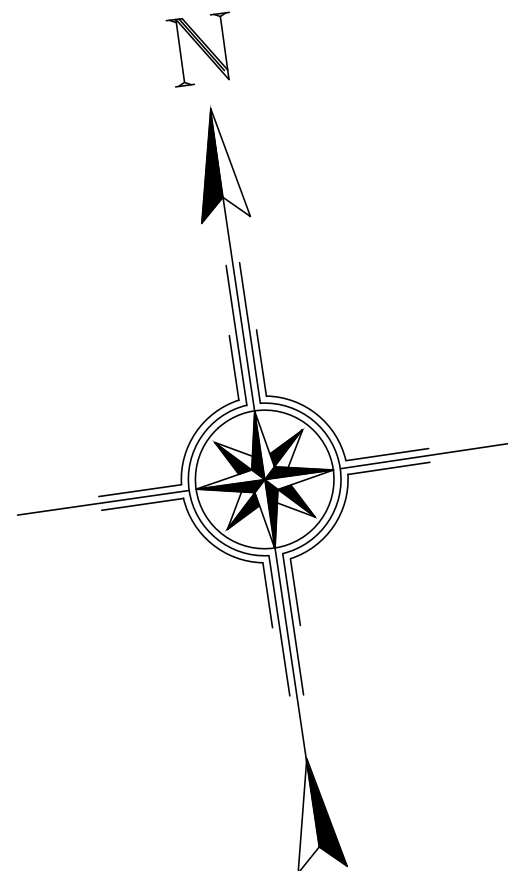

- LEGENDA
- MEIO FIO EXISTENTE
 - MEIO FIO PROJETADO
 - ESTAQUEAMENTO
 - MURO PROJETADO
 - ÁREA A SER PAVIMENTADA
 - SENTIDO DO ESCOAMENTO

ISS-P	ISS-C
CREA	APROVO
PROPRIETÁRIO	
PROJETO	
CONSTRUÇÃO	

TERMACO – TERMINAL LOGÍSTICO E OPERACIONAL PORTUÁRIO			
SÃO GONÇALO DO AMARANTE – PECÉM			
PRANCHA No.	DRENAGEM, TERRAPLENAGEM e PAVIMENTAÇÃO		
01/10	PLANTA BAIXA – SISTEMA VIÁRIO		
ESCALA:	DATA:	DESENHO:	PROJETO:
1:750	NOV./2023		