



QUADRO DE JANELAS - FITNESS			
ESQUADRIA	LARGURA	ALTURA	PEITORIL
JA1	0.600	0.600	1.800
JA3	1.800	0.400	1.100
JA4	2.400	0.600	1.600
JA5	1.800	0.600	1.600
JA7	3.600	0.600	1.800

CONSTRUÇÃO

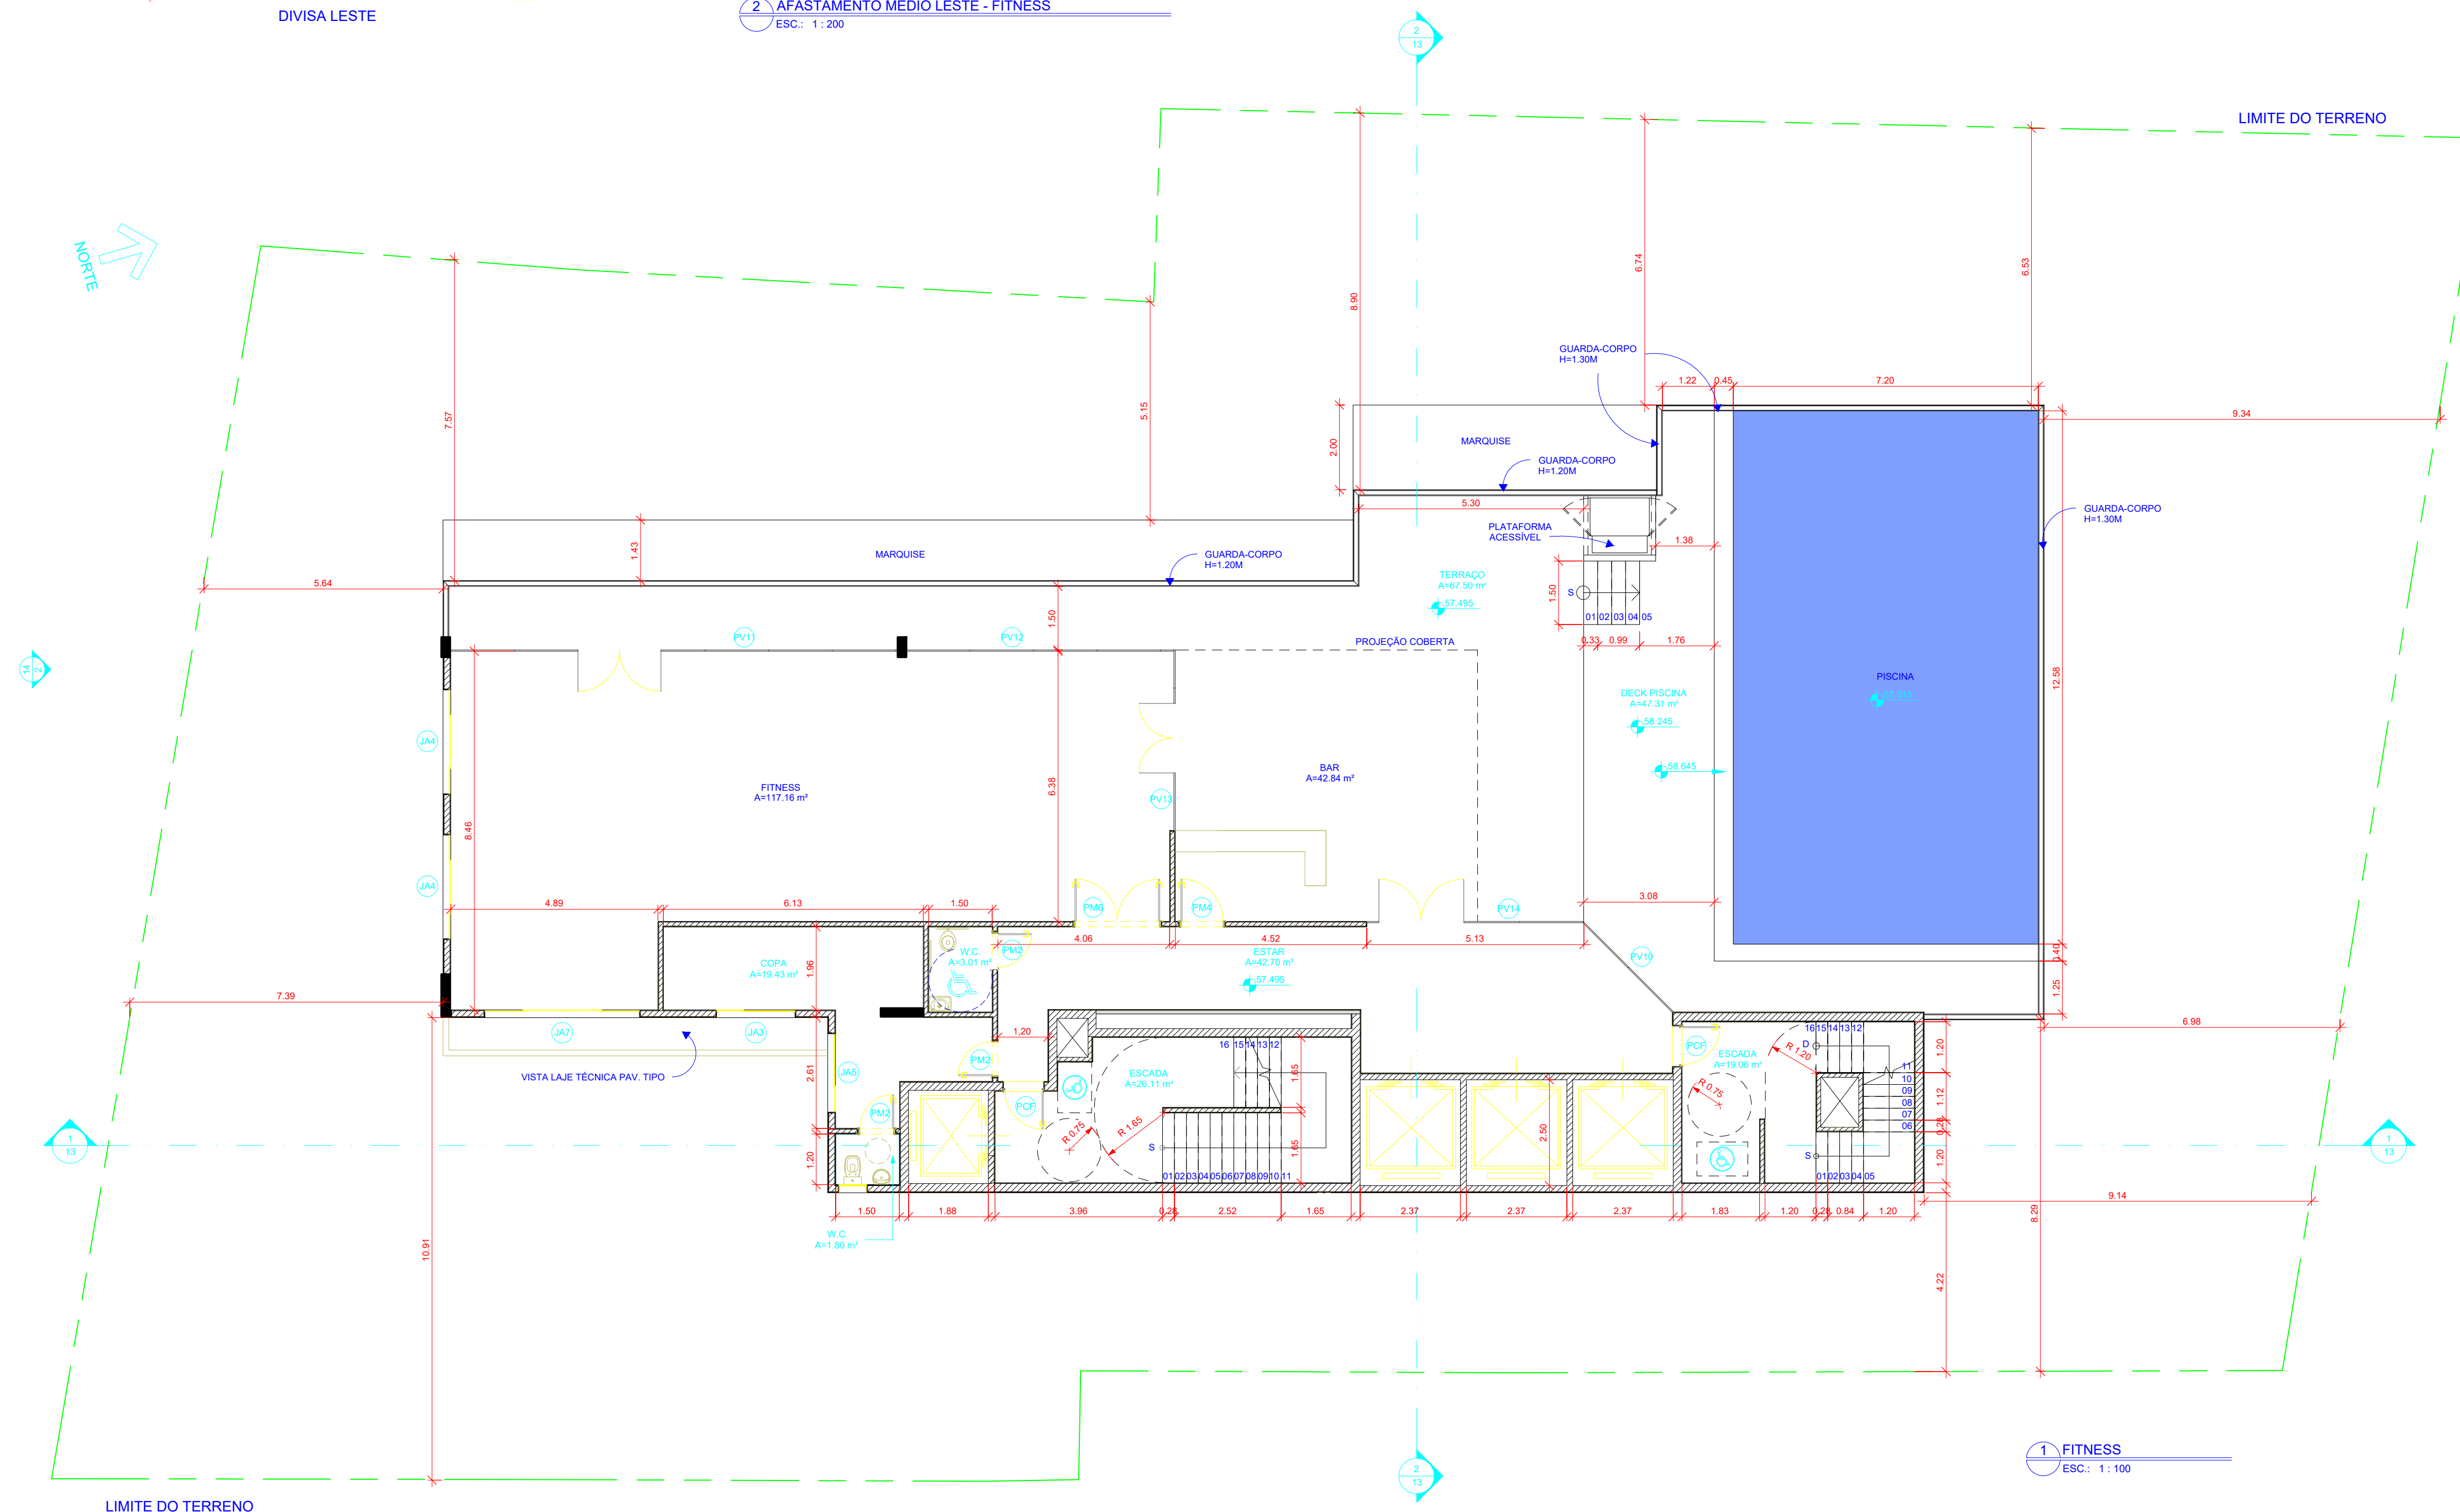

11 FITNESS
DATA: 08/11/2017 17:10:15
PROJ.: 14-009

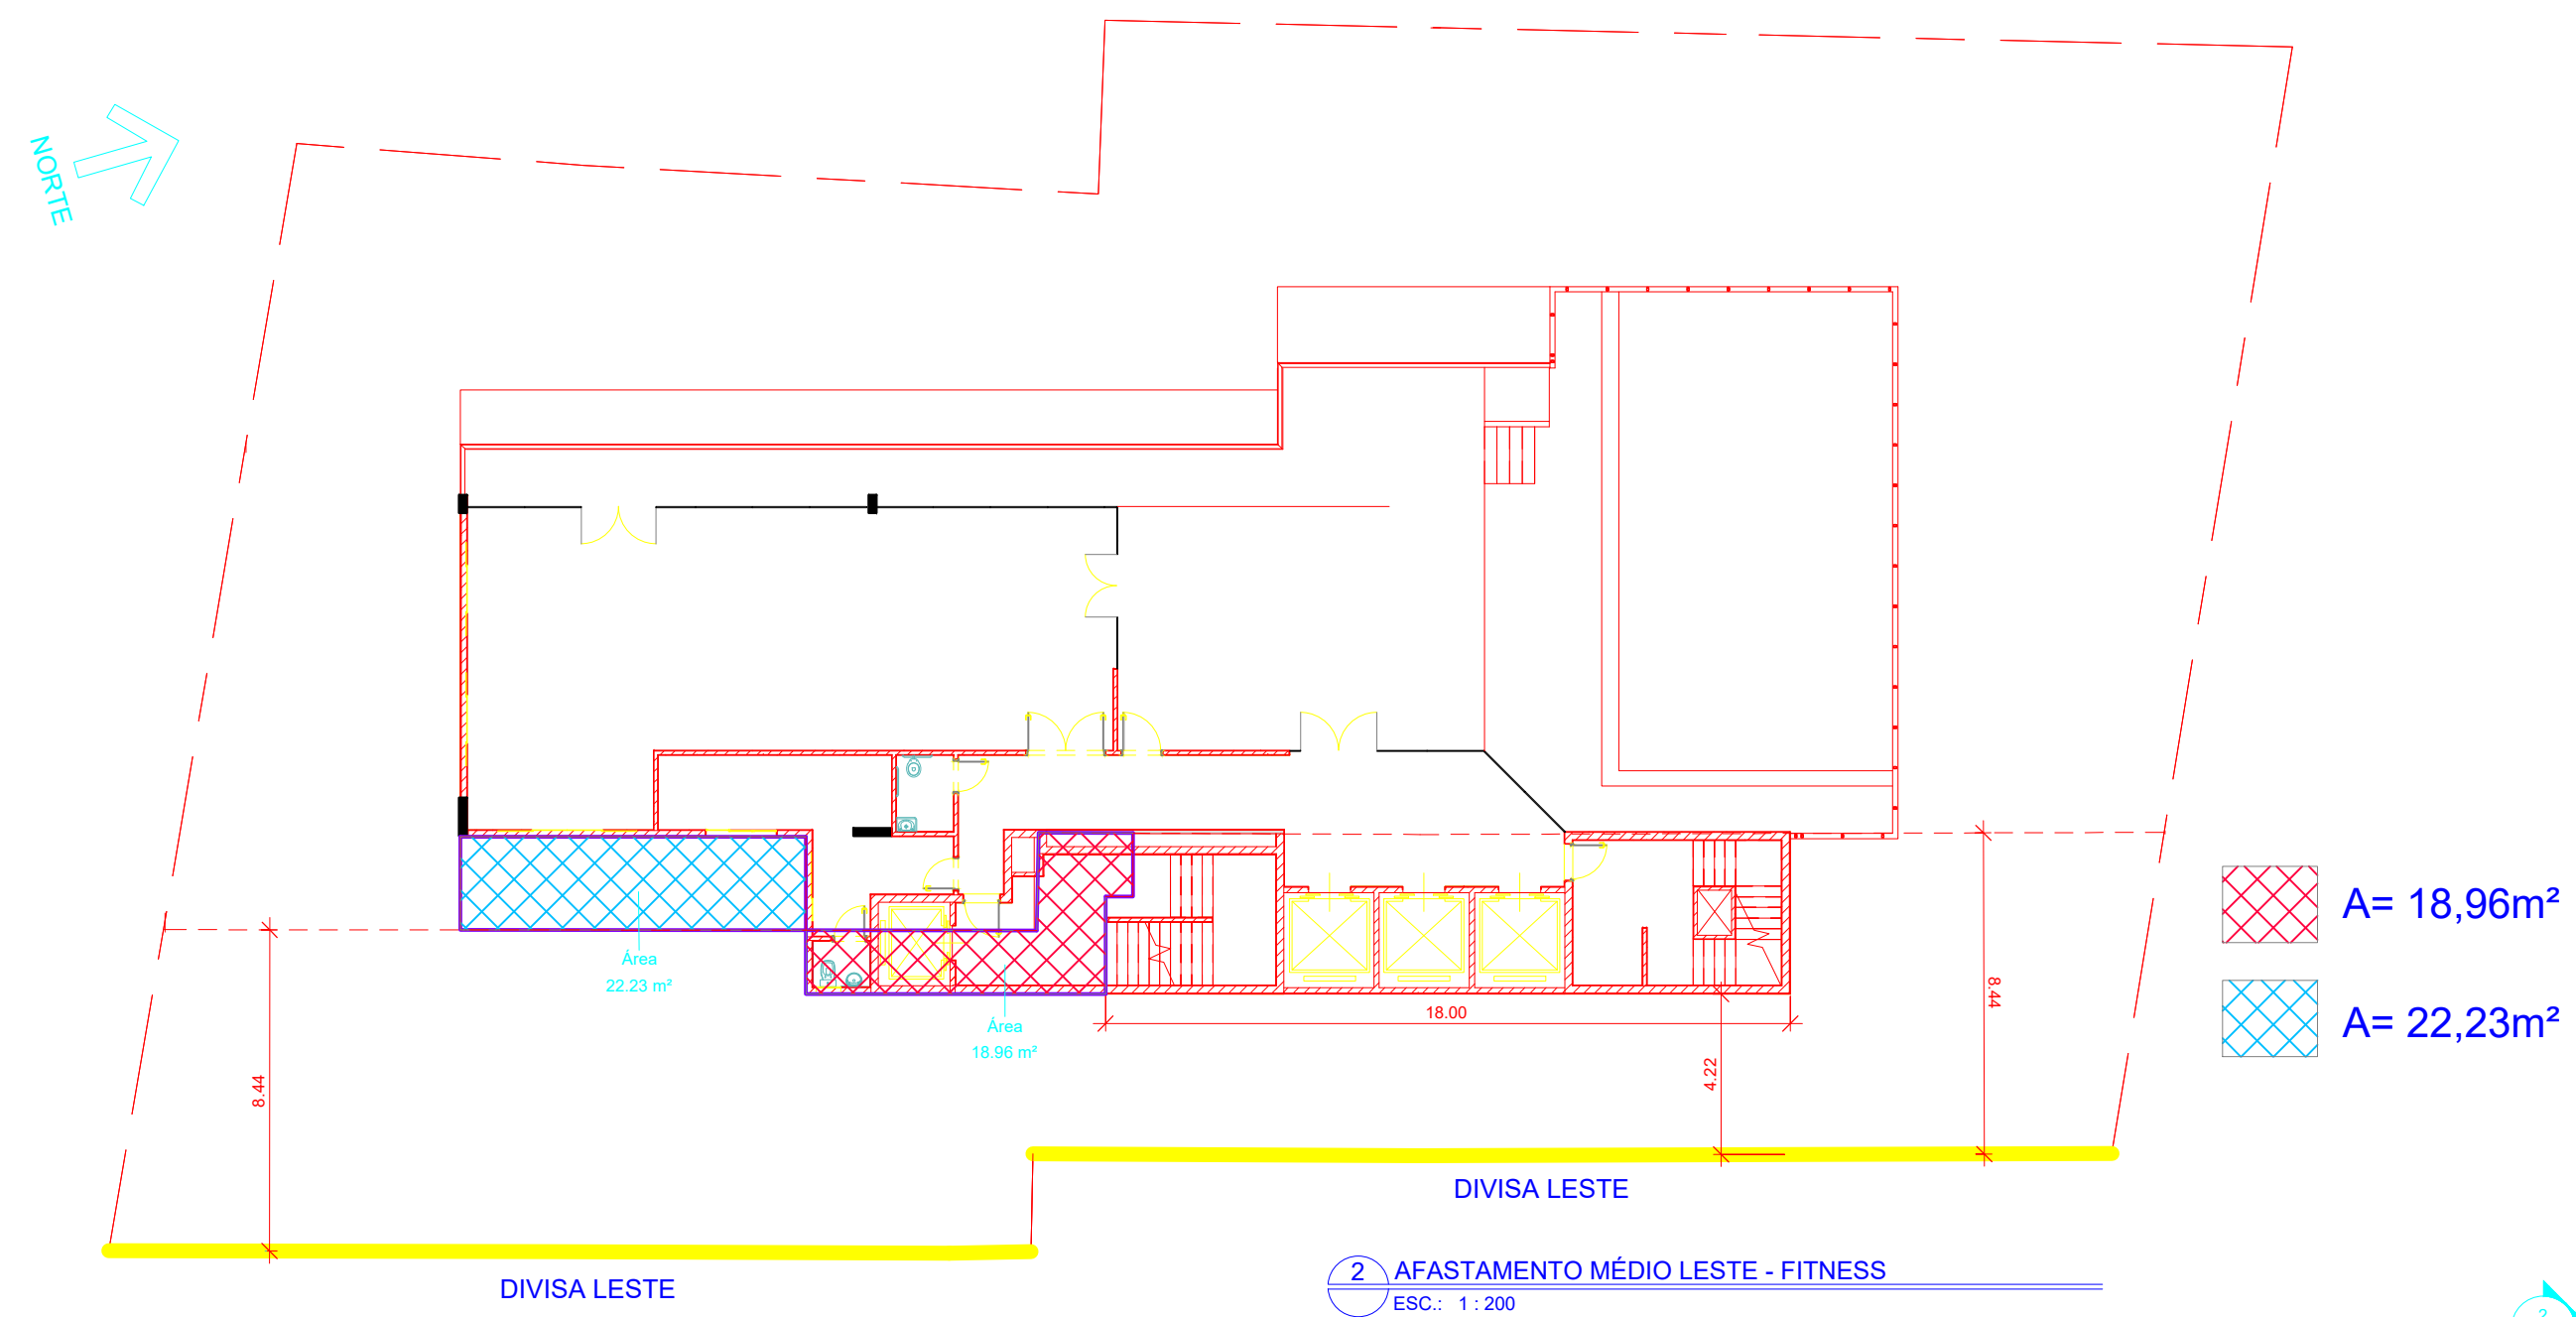